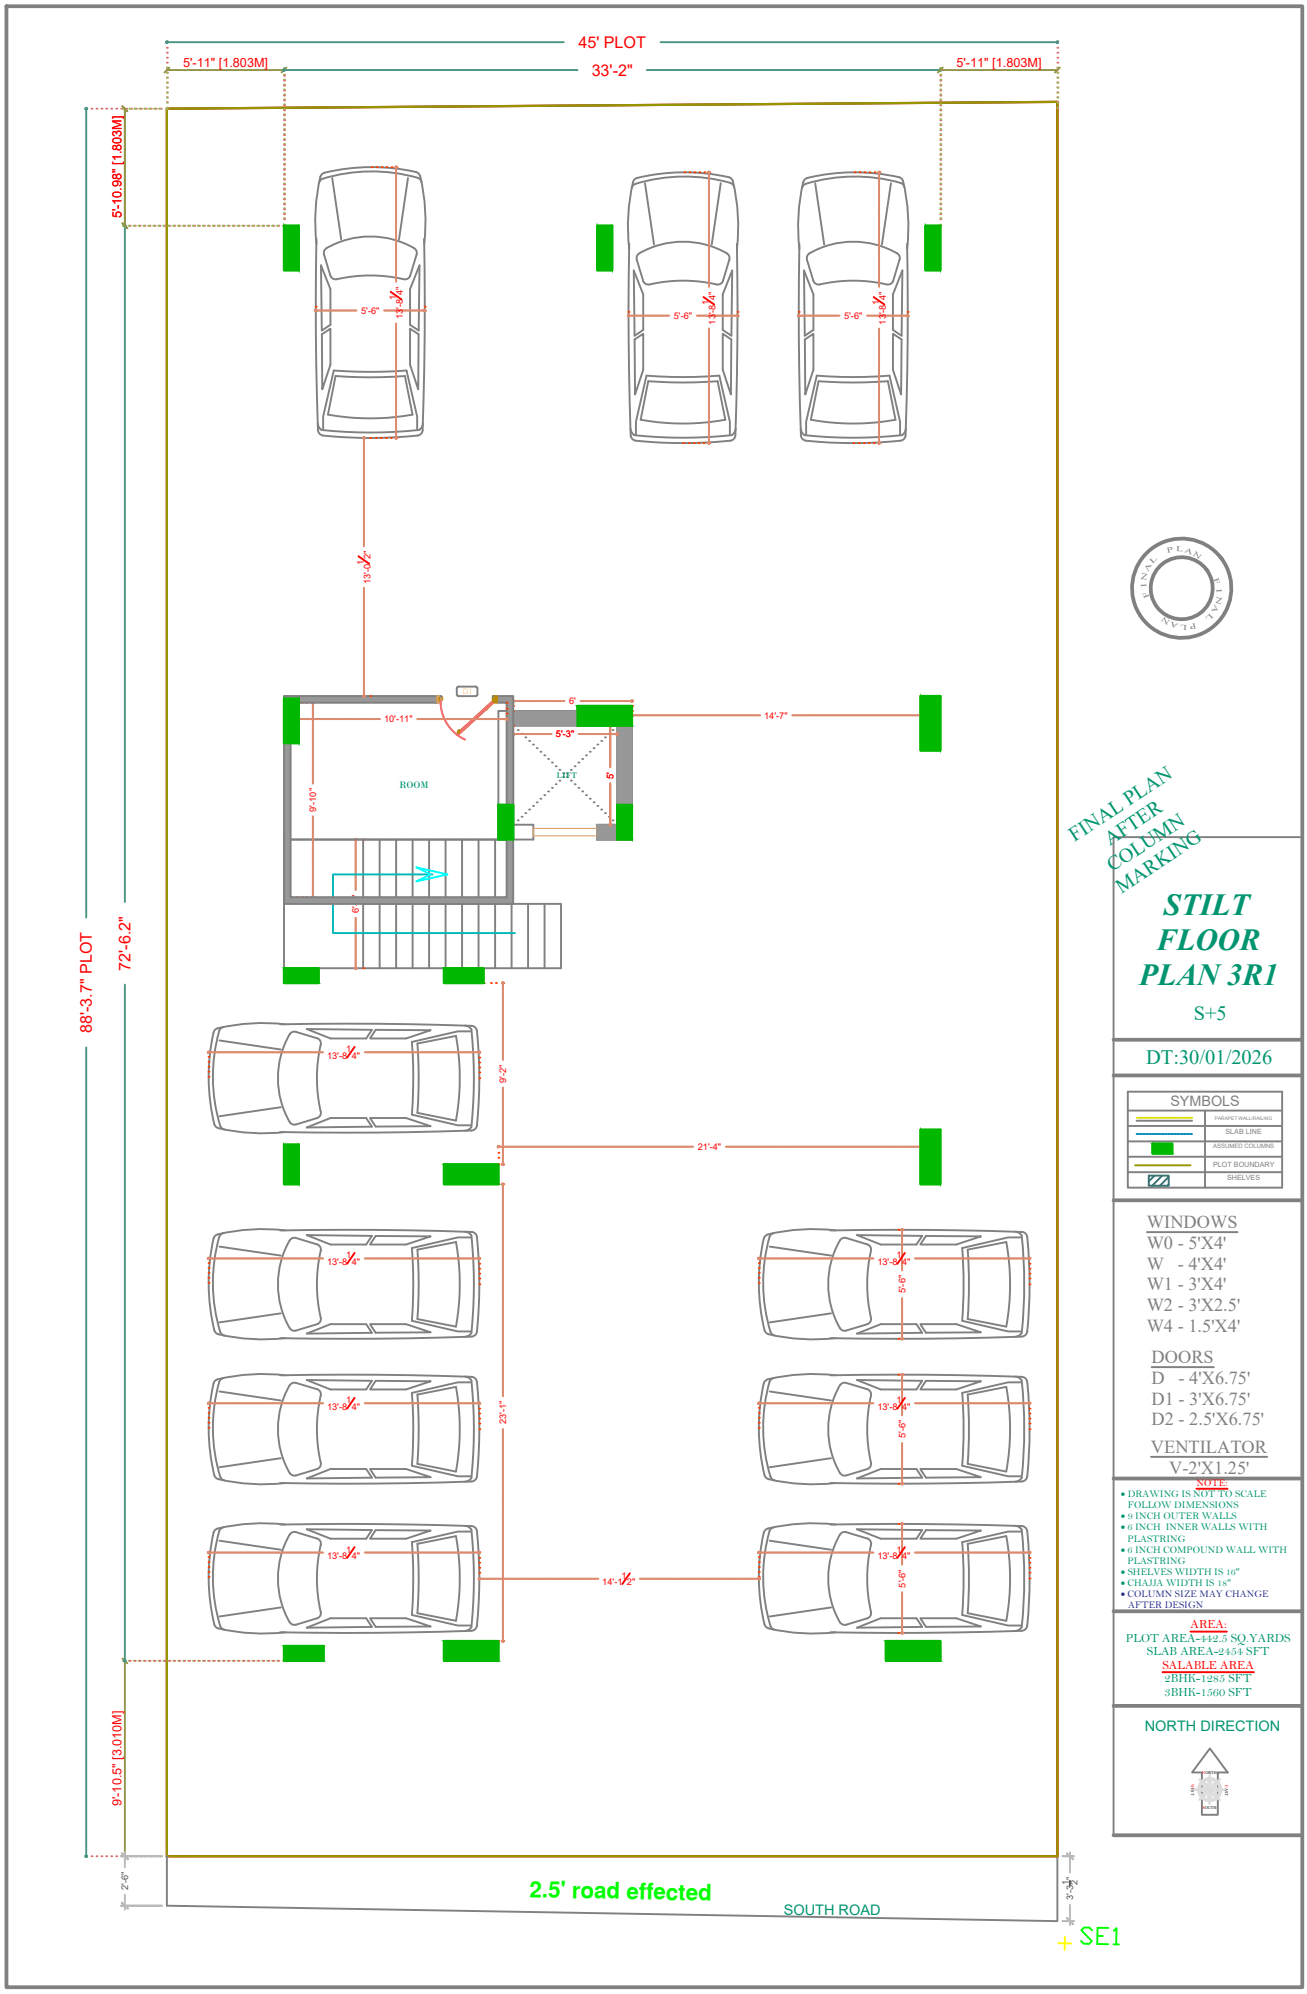
45' PLOT
33'-2"
5'-11" [1.803M]
5'-11" [1.803M]
5'-10.98" [1.803M]
88'-3.7" PLOT
72'-6.2"
9'-10.5" [3.010M]
5'-6"
13'-8¼"
13'-3½"
10'-11"
6'
5'-3"
14'-7"
ROOM
LIFT
9'-10"
5'
6'
9'-2"
21'-4"
23'-1"
14'-½"
2'-6"
3'-3½"
2.5' road effected
SOUTH ROAD
SE1
FINAL PLAN AFTER COLUMN MARKING
STILT FLOOR PLAN 3R1
S+5
DT:30/01/2026
SYMBOLS
PARAPET WALL/RAILING
SLAB LINE
ASSUMED COLUMNS
PLOT BOUNDARY
SHELVES
WINDOWS
W0 - 5'X4'
W - 4'X4'
W1 - 3'X4'
W2 - 3'X2.5'
W4 - 1.5'X4'
DOORS
D - 4'X6.75'
D1 - 3'X6.75'
D2 - 2.5'X6.75'
VENTILATOR
V-2'X1.25'
NOTE:
• DRAWING IS NOT TO SCALE FOLLOW DIMENSIONS
• 9 INCH OUTER WALLS
• 6 INCH INNER WALLS WITH PLASTRING
• 6 INCH COMPOUND WALL WITH PLASTRING
• SHELVES WIDTH IS 16"
• CHAJJA WIDTH IS 18"
• COLUMN SIZE MAY CHANGE AFTER DESIGN
AREA:
PLOT AREA-442.5 SQ.YARDS
SLAB AREA-2454 SFT
SALABLE AREA
2BHK-1285 SFT
3BHK-1560 SFT
NORTH DIRECTION

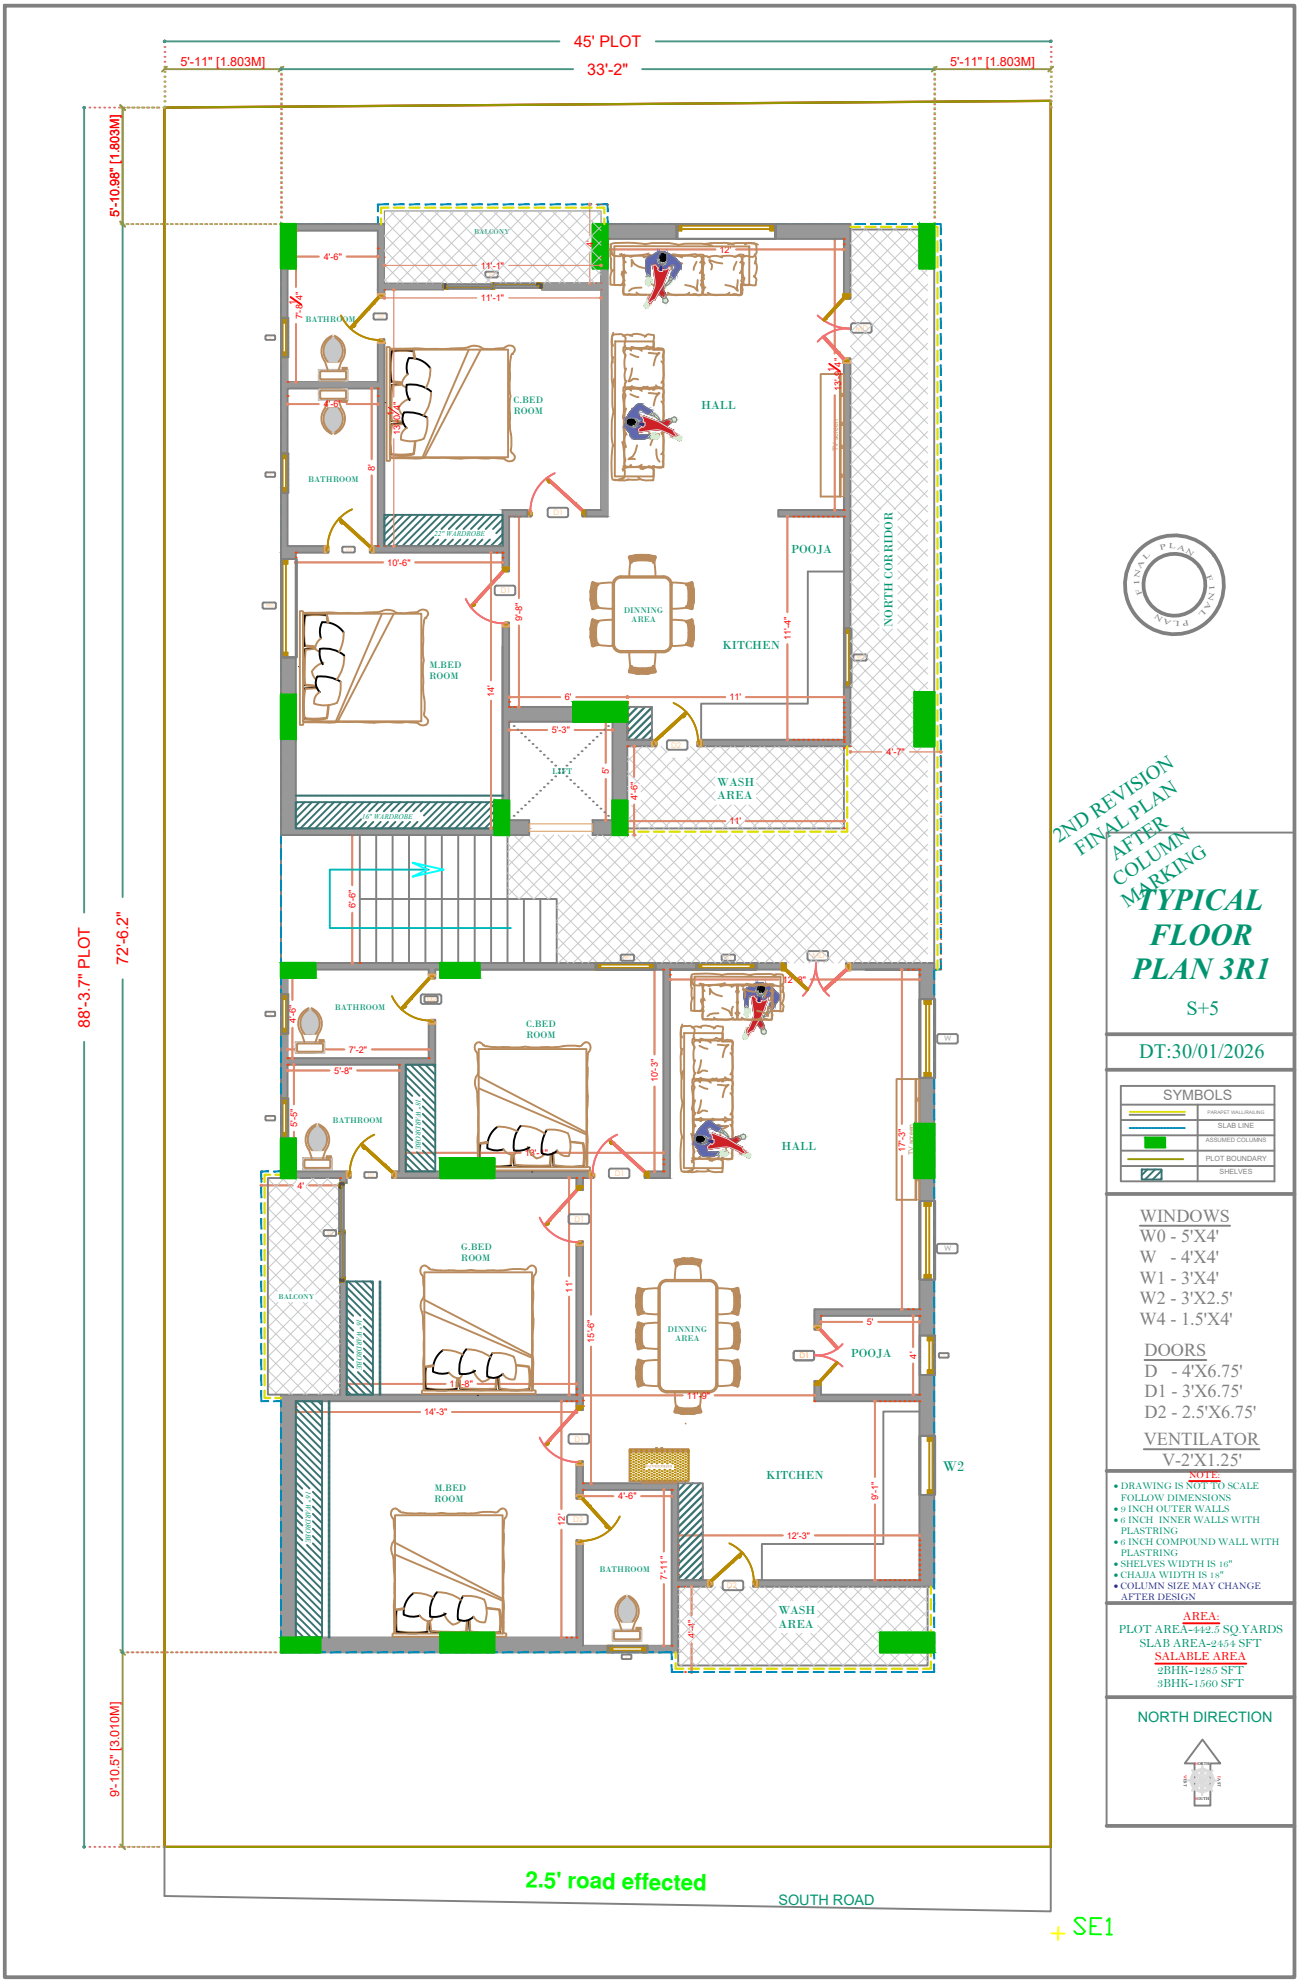
45' PLOT
33'-2"
5'-11" [1.803M]
5'-11" [1.803M]
5'-10.98" [1.803M]
88'-3.7" PLOT
72'-6.2"
9'-10.5" [3.010M]
BALCONY
BATHROOM
C.BED ROOM
HALL
POOJA
NORTH CORRIDOR
DINNING AREA
KITCHEN
M.BED ROOM
WASH AREA
LIFT
G.BED ROOM
W2
2.5' road effected
SOUTH ROAD
SE1
2ND REVISION FINAL PLAN AFTER COLUMN MARKING
TYPICAL FLOOR PLAN 3R1
S+5
DT:30/01/2026
SYMBOLS
PARAPET WALL/RAILING
SLAB LINE
ASSUMED COLUMNS
PLOT BOUNDARY
SHELVES
WINDOWS
W0 - 5'X4'
W - 4'X4'
W1 - 3'X4'
W2 - 3'X2.5'
W4 - 1.5'X4'
DOORS
D - 4'X6.75'
D1 - 3'X6.75'
D2 - 2.5'X6.75'
VENTILATOR
V-2'X1.25'
NOTE:
• DRAWING IS NOT TO SCALE FOLLOW DIMENSIONS
• 9 INCH OUTER WALLS
• 6 INCH INNER WALLS WITH PLASTRING
• 6 INCH COMPOUND WALL WITH PLASTRING
• SHELVES WIDTH IS 16"
• CHAJJA WIDTH IS 18"
• COLUMN SIZE MAY CHANGE AFTER DESIGN
AREA:
PLOT AREA-442.5 SQ YARDS
SLAB AREA-2454 SFT
SALABLE AREA
2BHK-1285 SFT
3BHK-1560 SFT
NORTH DIRECTION